

מס	מהות השינוי

התוכנית היא רכוש המוזיאון
אין לעשות בהן כל שימוש שלא
למטרה לשמה נמסרו למזמין

המבצע יהיה אחראי לבדיקת
התאמתן של התוכניות לשטח
המבצע אחראי על בקרת המידות
ועליו להודיע למתכנן על כל
טעות או אי התאמה

יש להתייחס אך ורק למידות
המצויינות בשרטוט- אין למדוד על
גבי השרטוט

שם הפרויקט

EN-2.3-060

שם השרטוט

0523503898

איל פוגל

eyalv@mada.org

מתכנן

מוזיאון המדע ע"ש בלומפילד

שדרות המוזאונים
גבעת רם ירושלים

<https://www.mada.org.il/>



24/08/2025


ק"מ: 1:20

מידות ב"מ


A4

SHEET 1 OF 2



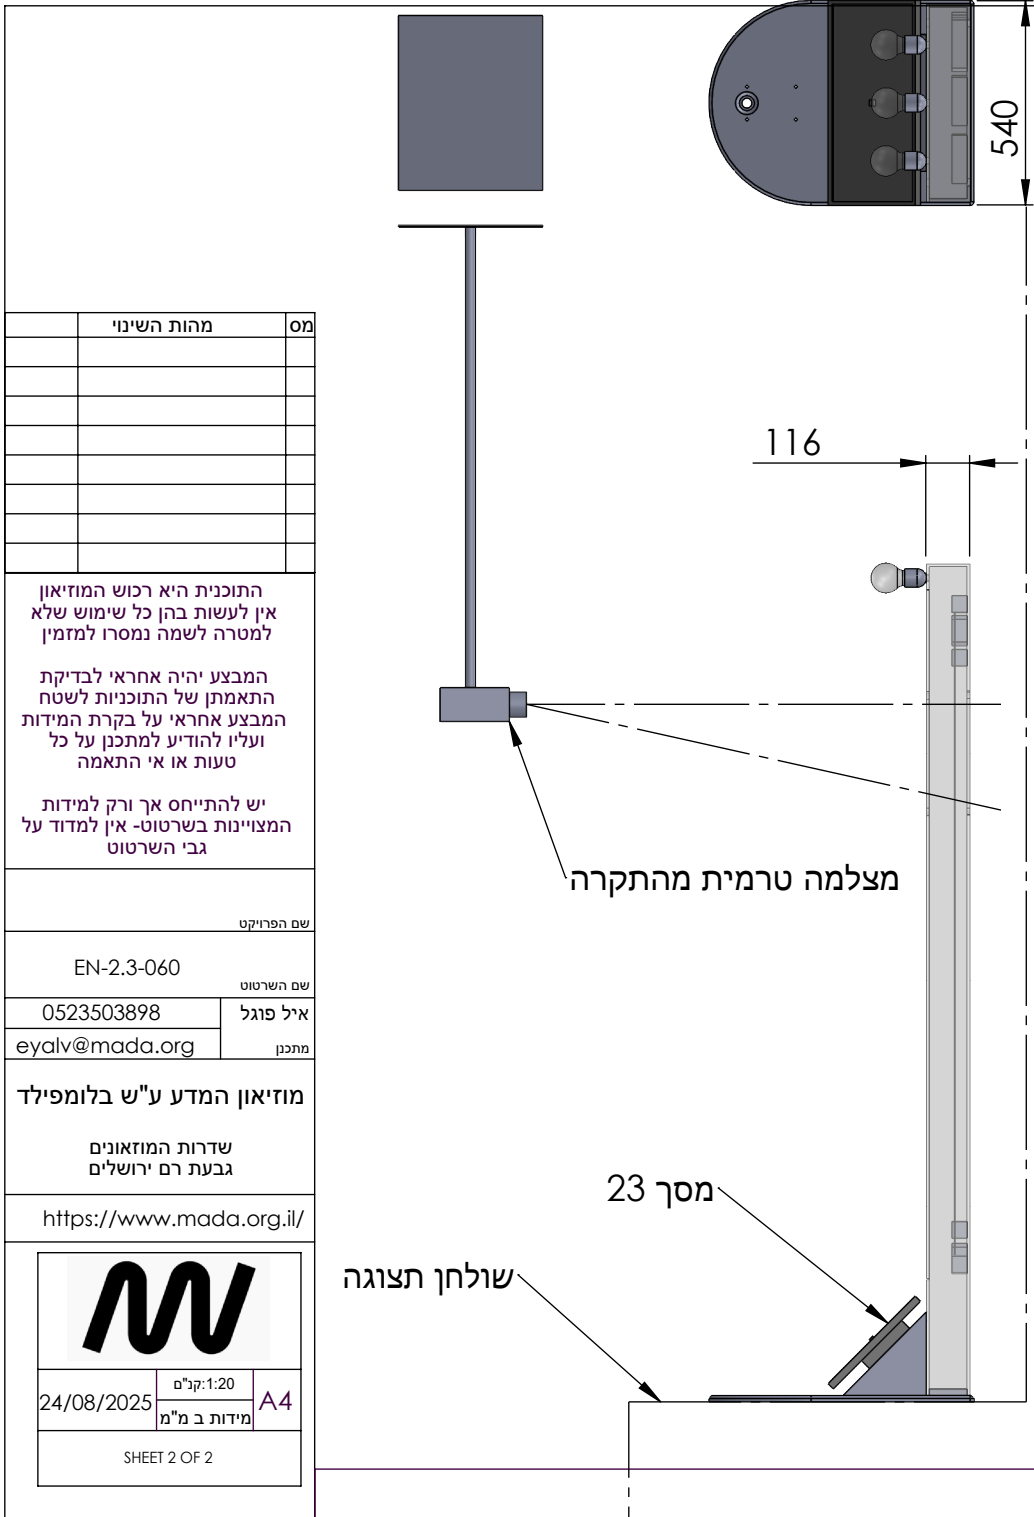

7seg

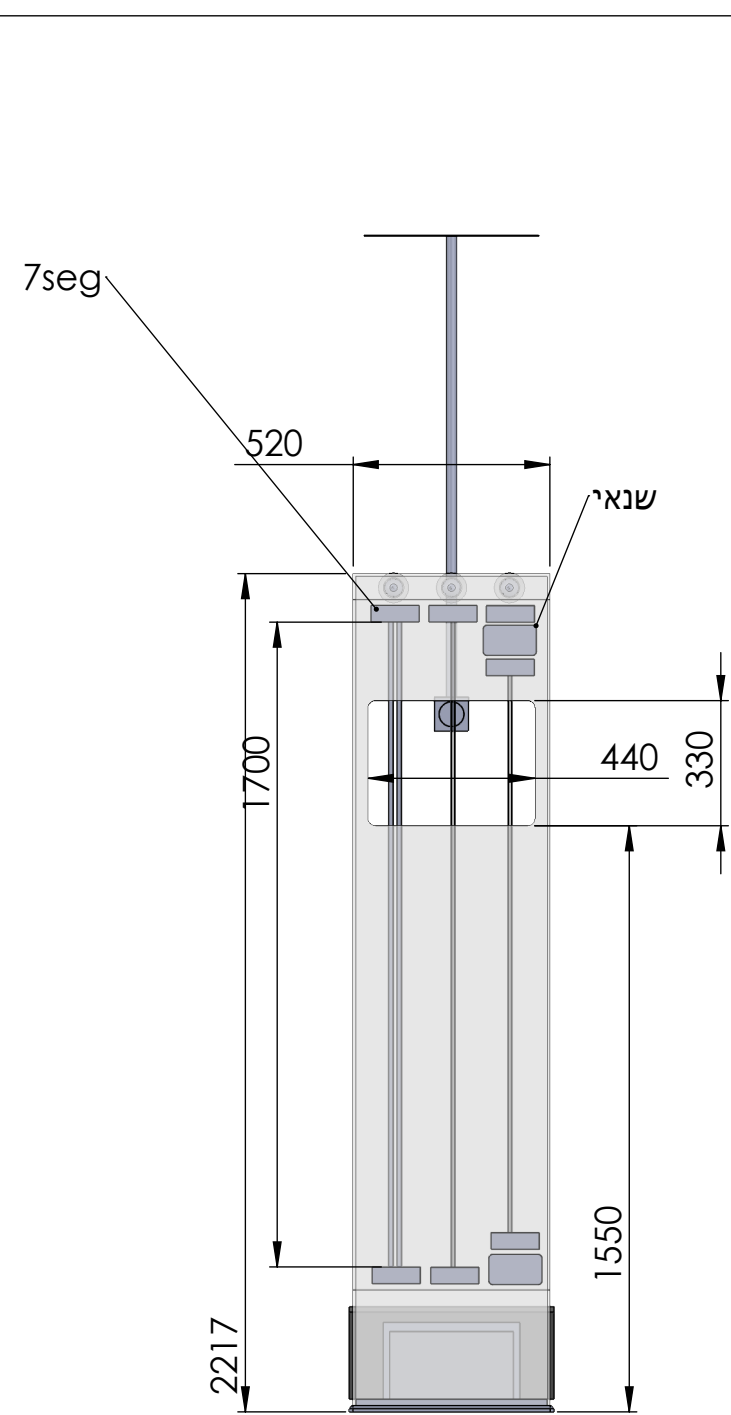

מס	מהות השינוי
התוכנית היא רכוש המוזיאון אין לעשות בהן כל שימוש שלא למטרה לשמה נמסרו למזמין	
המבצע יהיה אחראי לבדיקת התאמתן של התוכניות לשטח המבצע אחראי על בקרת המידות ועליו להודיע למתכנן על כל טעות או אי התאמה	
יש להתייחס אך ורק למידות המצויינות בשרטוט- אין למדוד על גבי השרטוט	
שם הפרויקט	
EN-2.3-060	
שם השרטוט	איל פוגל
0523503898	
eyalv@mada.org	מתכנן
מוזיאון המדע ע"ש בלומפילד	
שדרות המוזאונים גבעת רם ירושלים	
https://www.mada.org.il/	
24/08/2025	מ"ק: 1:20
מידות ב מ"מ	A4
SHEET 2 OF 2	